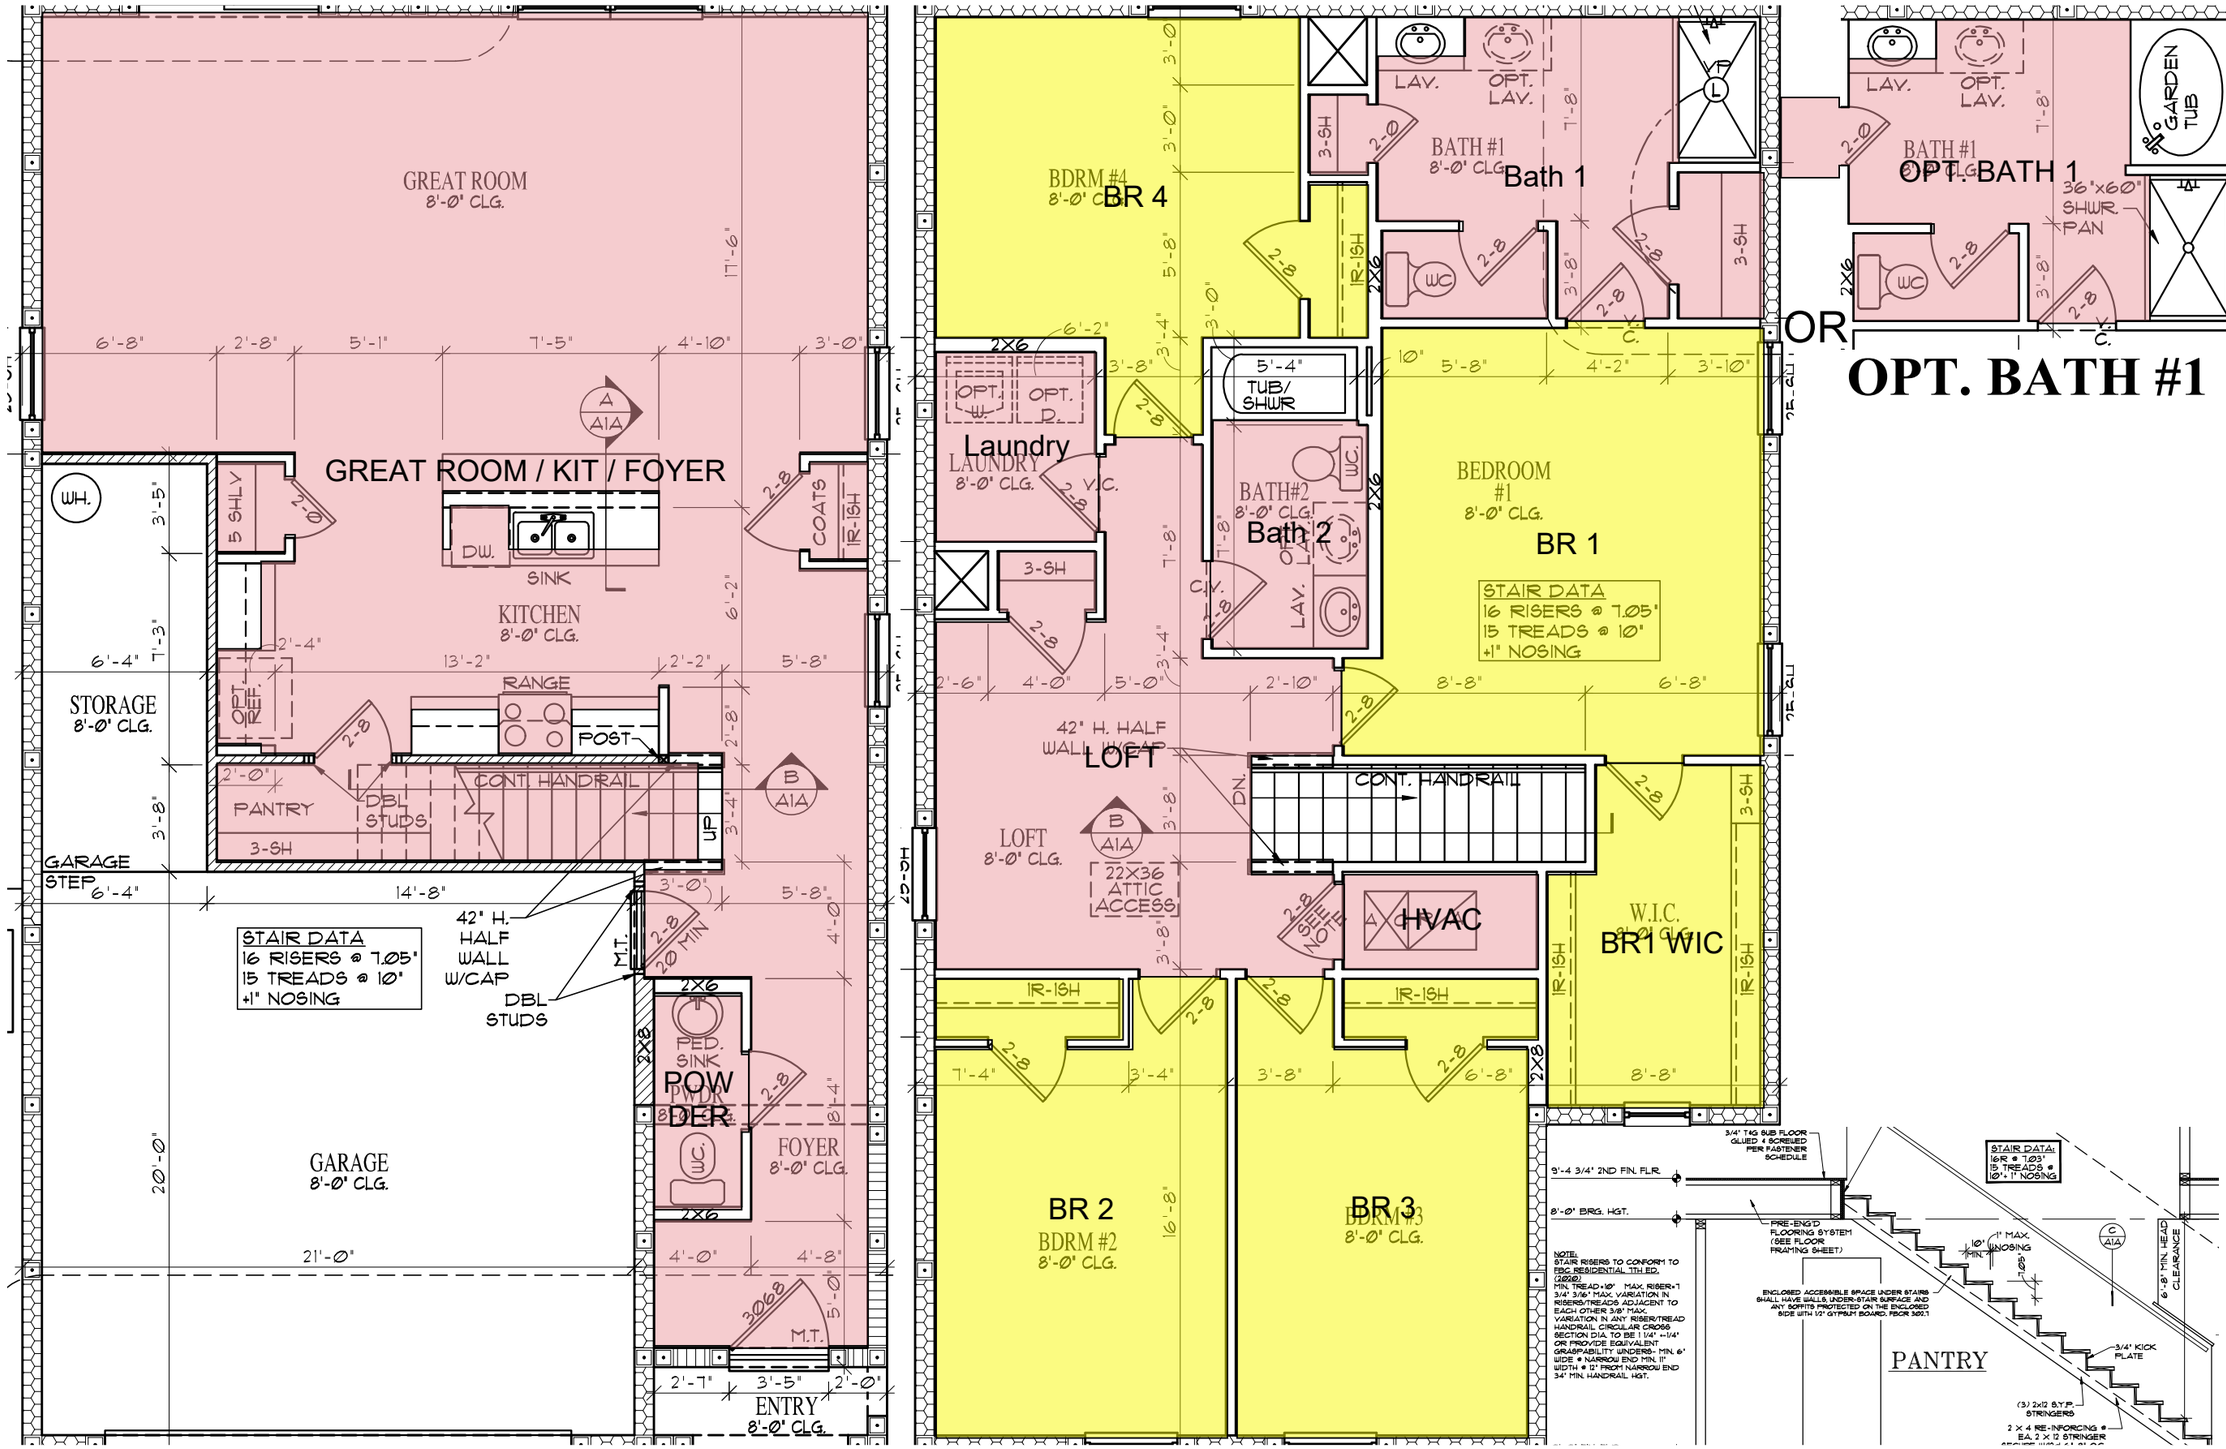

12' Carpet 150' Floor Tile: Tile

PADDING:
89.33 SY

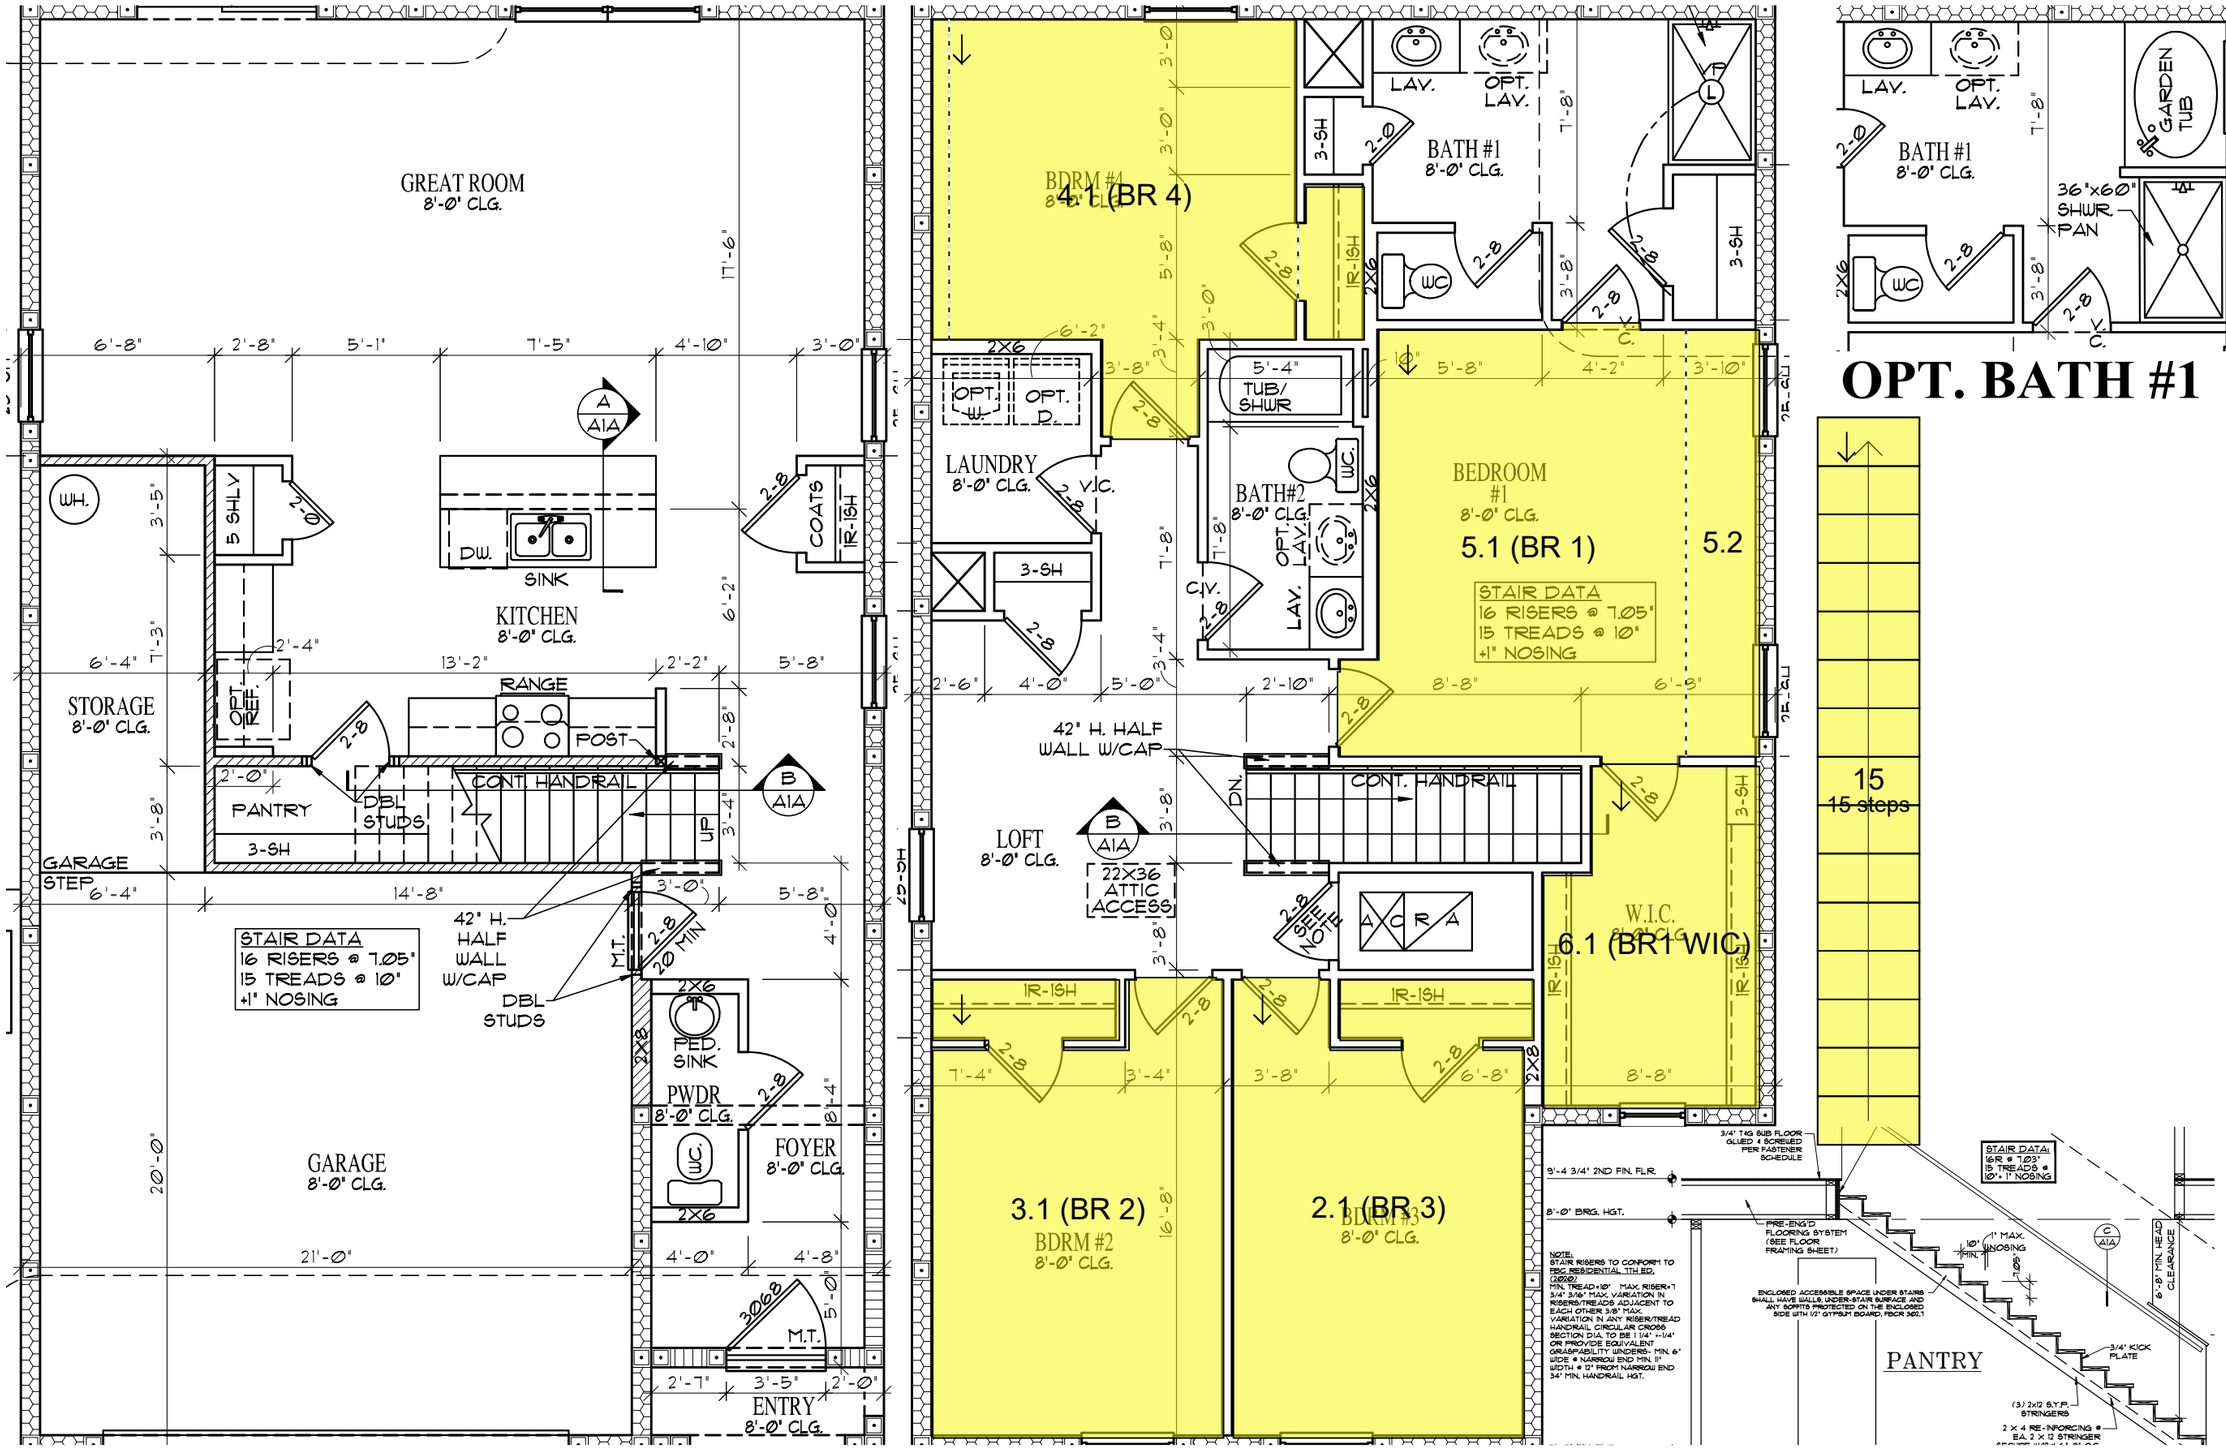

12' Carpet 150'

12 X 83' 6" 111.33 SY

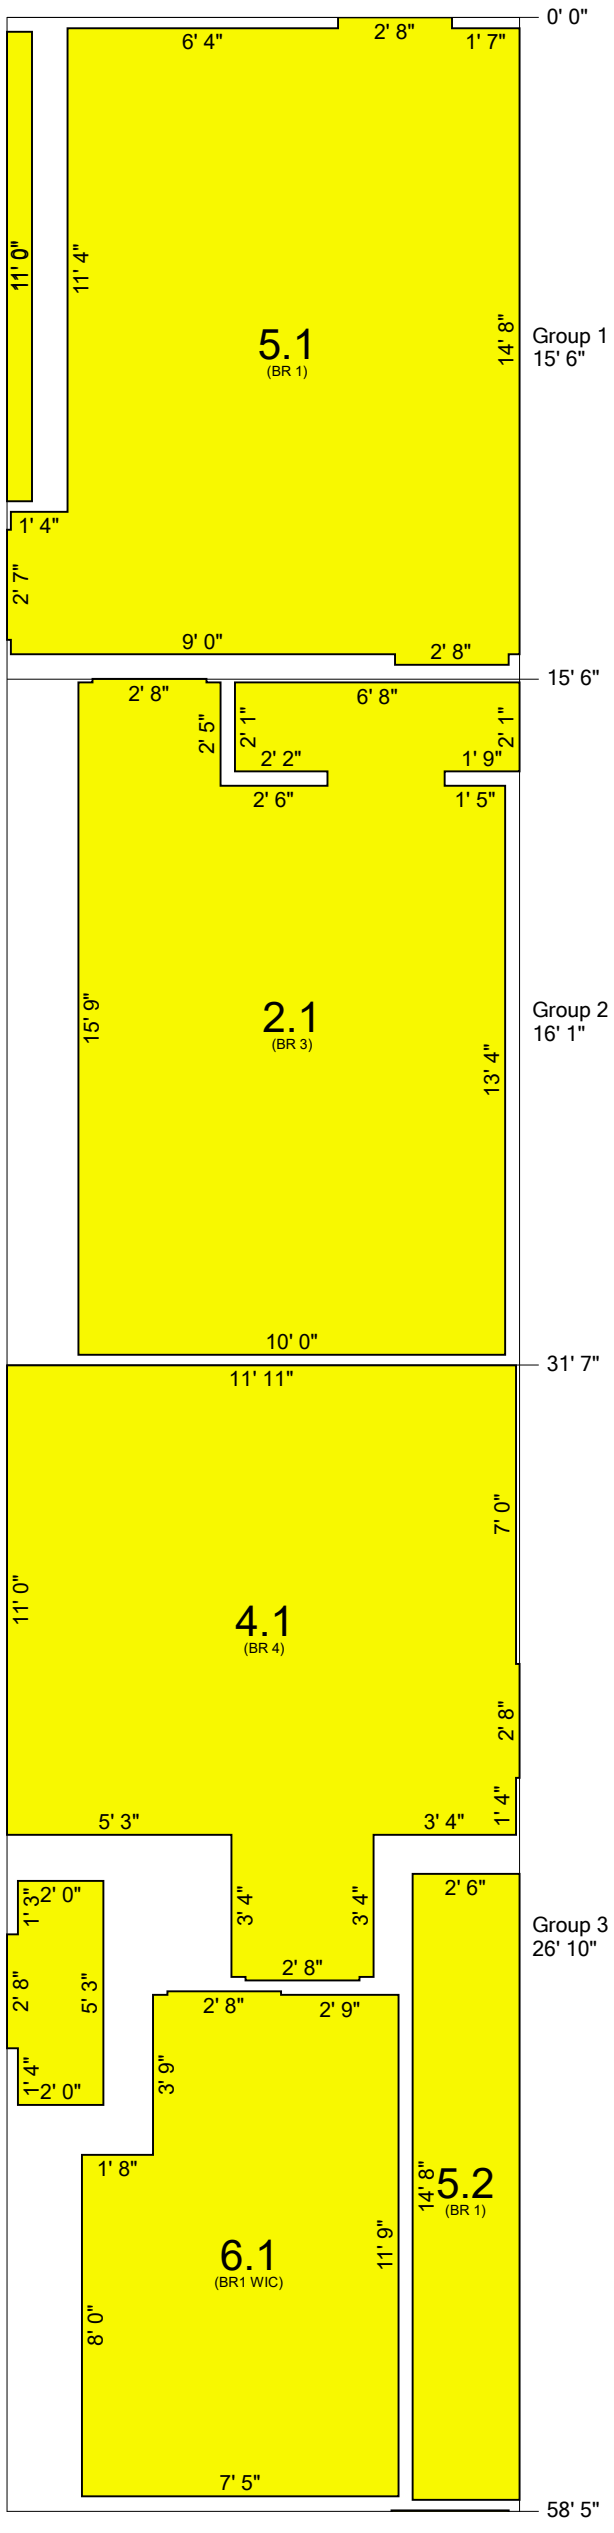

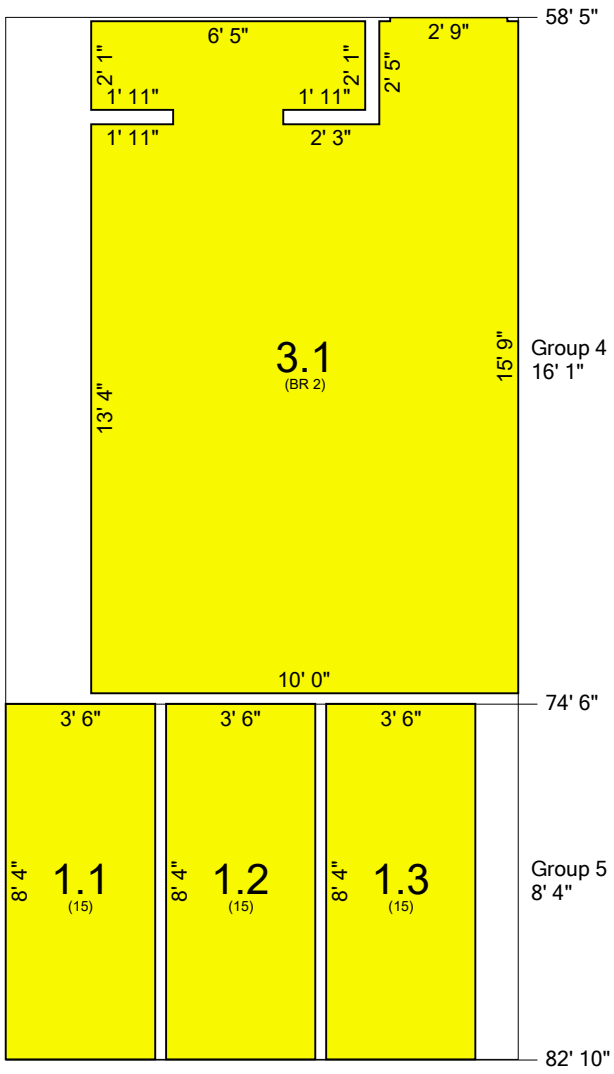

12' Carpet 150' 15.6% Waste (82' 10")

START OF ROLL System roll 1 (150' 0")

Group 1 - Begins at 0' 0"

5.1 (BR 1)
4.2 (BR 4)

End of Group 1 - Length: 15' 6"

Group 2 - Begins at 15' 6"

2.1 (BR 3)

End of Group 2 - Length: 16' 1"

Group 3 - Begins at 31' 7"

4.1 (BR 4)
4.3 (BR 4)
6.1 (BR1 WIC)
5.2 (BR 1)

End of Group 3 - Length: 26' 10"

Group 4 - Begins at 58' 5"

3.1 (BR 2)

End of Group 4 - Length: 16' 1"

Group 5 - Begins at 74' 6"

1.1 (15)
1.2 (15)
1.3 (15)

End of Group 5 - Length: 8' 4"

END OF ROLL